



Se uppställningsritningar för mer detaljerad information.

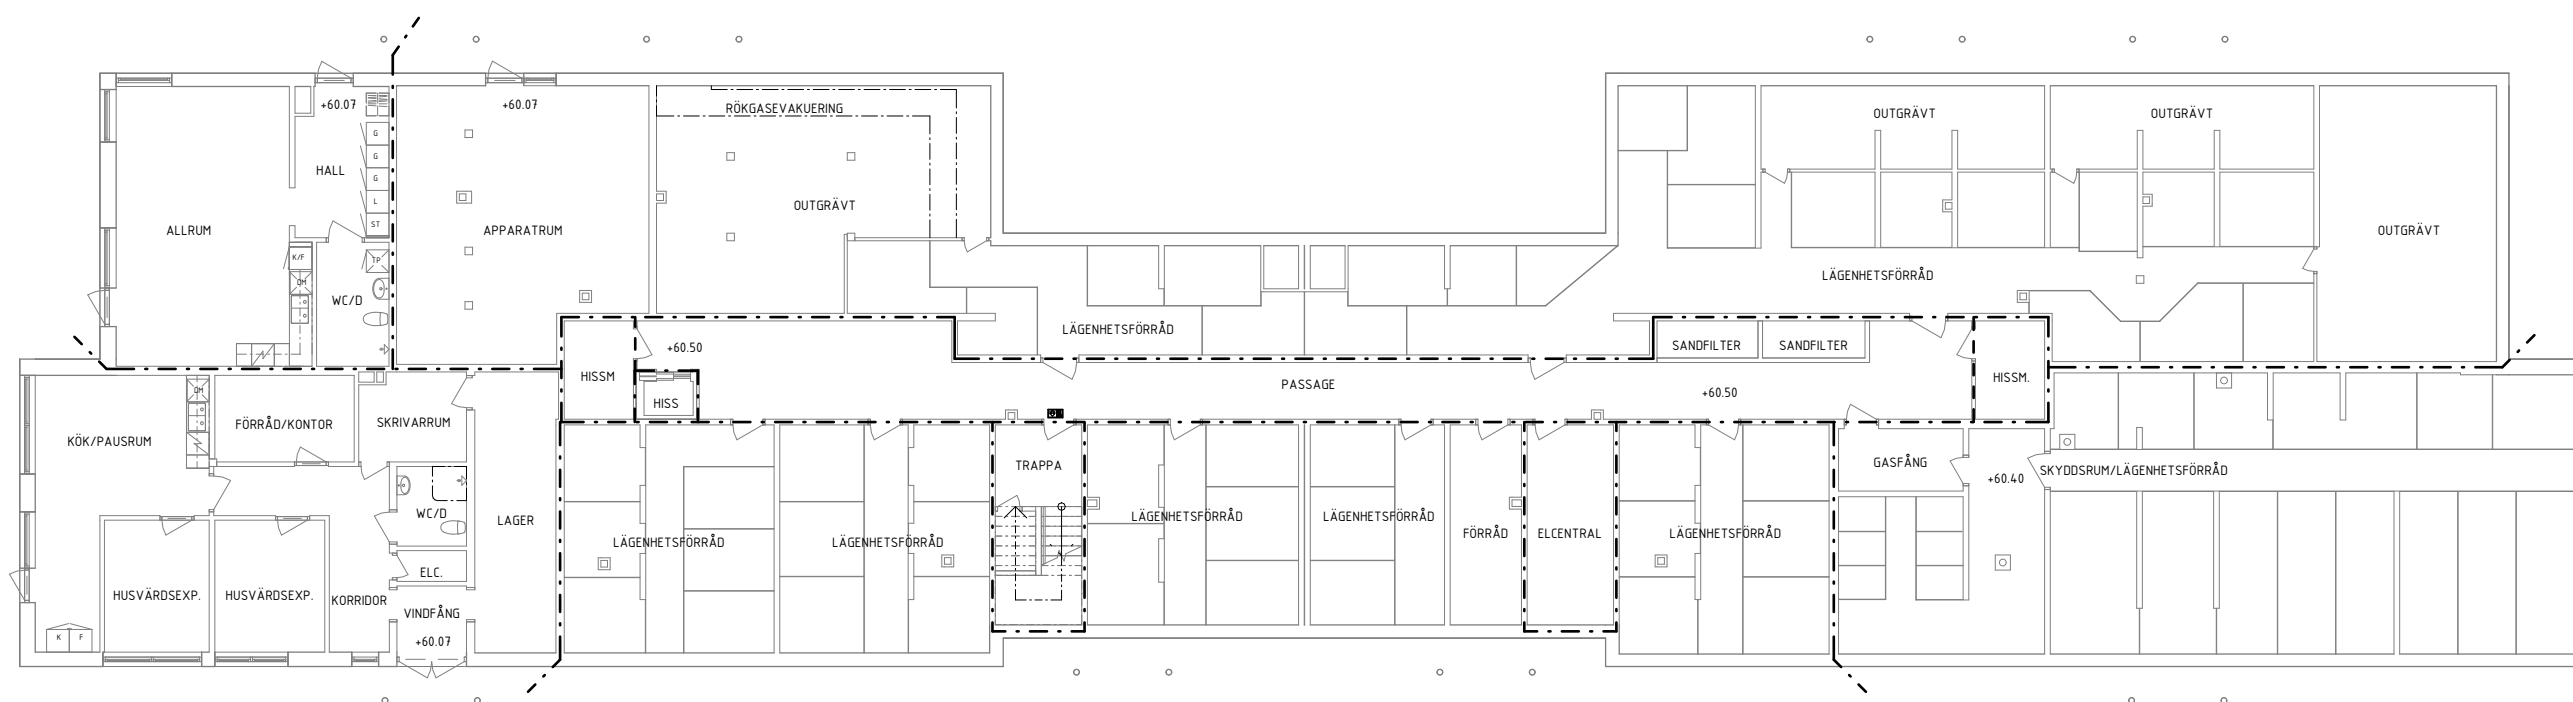

0 1 2 3 4 5 6 7 8 9 10m
SKALA 1:100

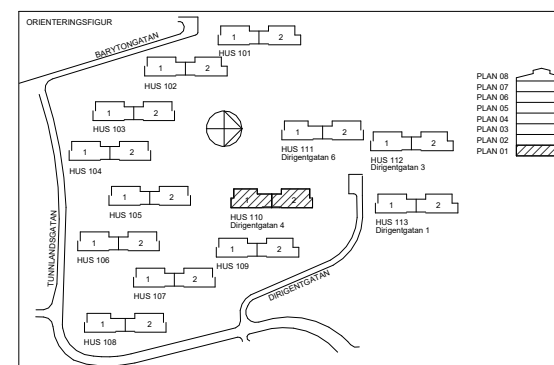

TOTALENTREPRENOR SKANSKA		010-448 00 00
		
BOSTADS AB POSEIDON		
Box 1 (Angered Torg 14) 424 21 Angered		
Orgnr: 556120-3398		
DISTRIKT: Väster, Mandolingatan 116		
PROJEKTNUMMER 906164	FASTIGHETSNUMMER 5837	
GATUADRESS Dirigentgatan 1, 3, 4, 6		

BET	ANBUDEN AVSR		DATUM	SIGN
BYGGHANDLING				
STAMRENOVERING KAVERÖS 4ST HUS				
JÄRNBROTT 154:1				
☒	A	STUDIO EKBERG AB	0709-36 06 90	
	AK	CEDÅS AKUSTIK	070-515 40 58	
	BR	AFRY	010-505 32 06	
	E	ESF SERVICE	031-54 54 22	
	VS	BENG T DAHLGREN	031-720 25 00	
	V	ENERGI & MILJÖTEKNIK	031-69 61 00	
URSPRUNGSARKITEKT GAKO Arkitektkontor				
UPPDRAG NR	RITAD/KONSTR AV		HANDLÄGGARE	
SKAD2501	PP		P PODDA	
DATUM	ANSVARIG			
2025-03-31	CHARLOTTE FLODIN			
ÖVERSIKTSPLAN				
HUS 110				
PLAN 01, KÄLLARPLAN				
CAD Revit	SKALA A1 1:100 A2 1:200	NUMMER A--40-1-1001000		BET