



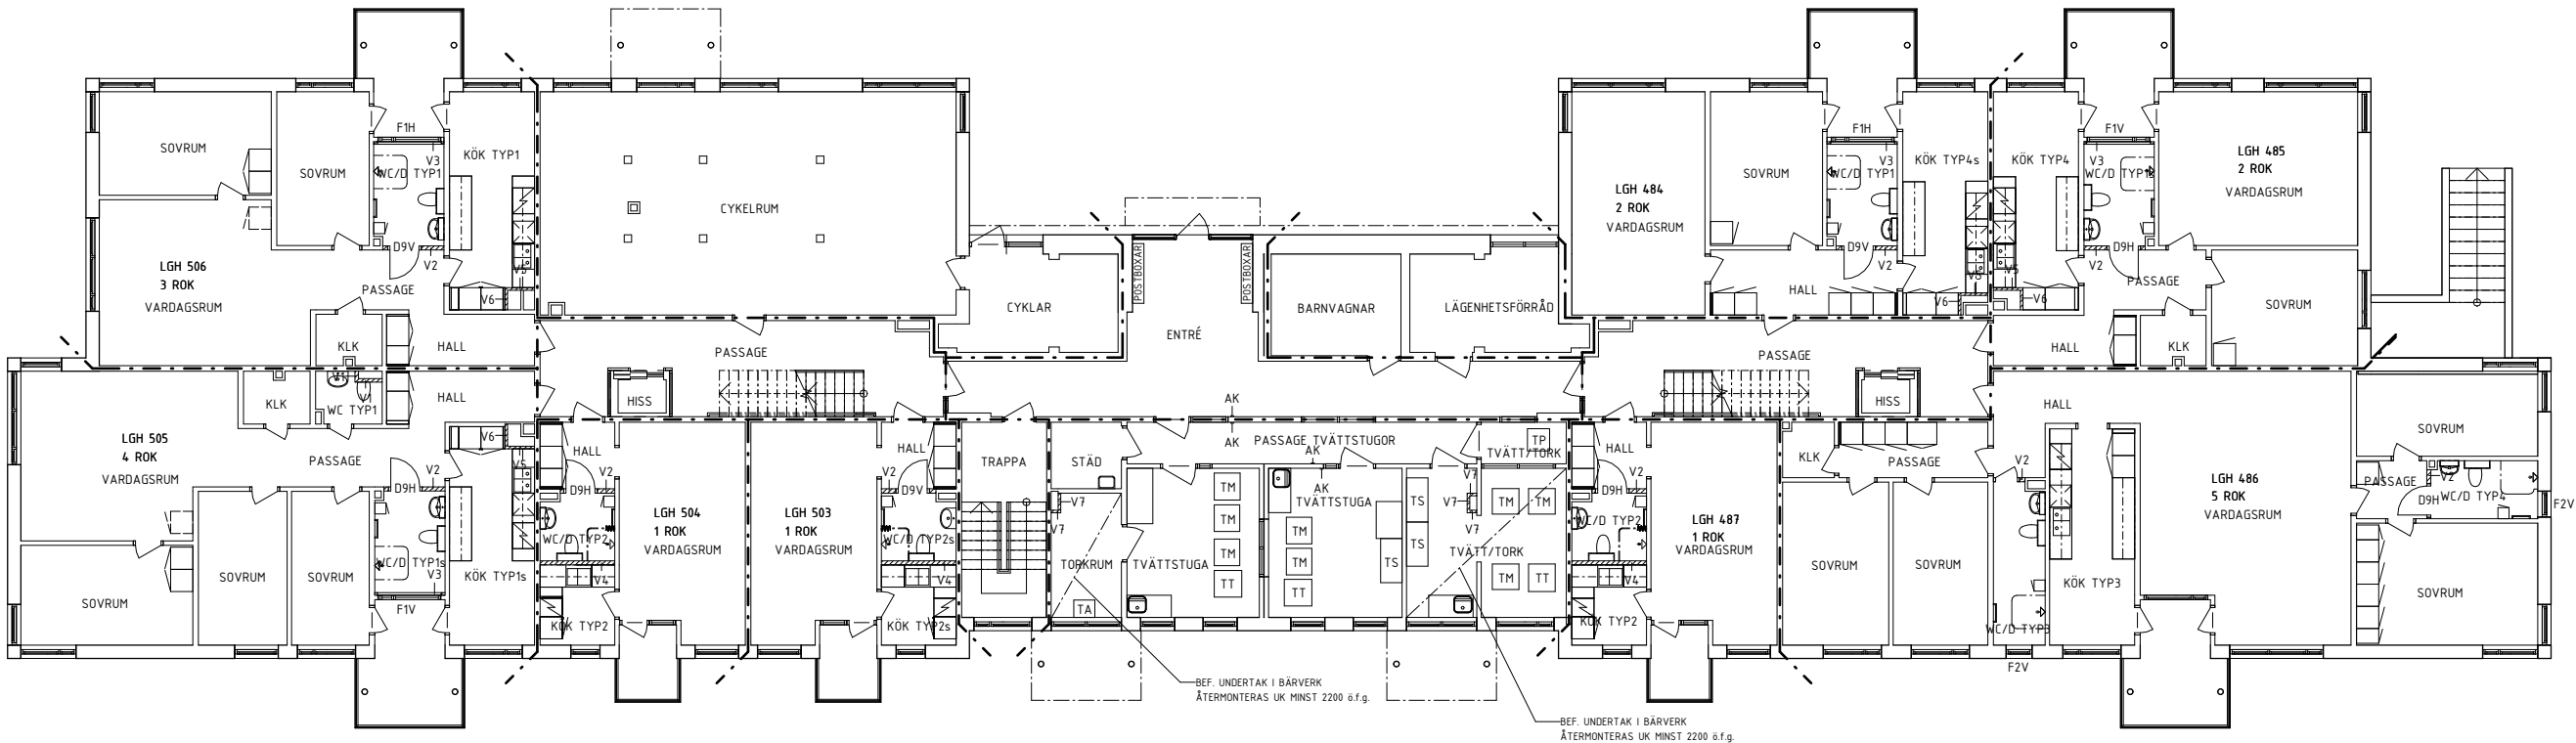

BEF. UNDERTAK I BÄRVERK
ÅTERMONTERAS UK MINST 2200 ö.f.g.

BEF. UNDERTAK I BÄRVERK
ÅTERMONTERAS UK MINST 2200 ö.f.g.

Handlingar är i huvudsak upprättade efter GAKO arkitektkontors handlingar från 1964 samt handlingar från Hofvenschiöld arkitekter AB från 2008. Avvikeler i mått och utförande kan förekomma.

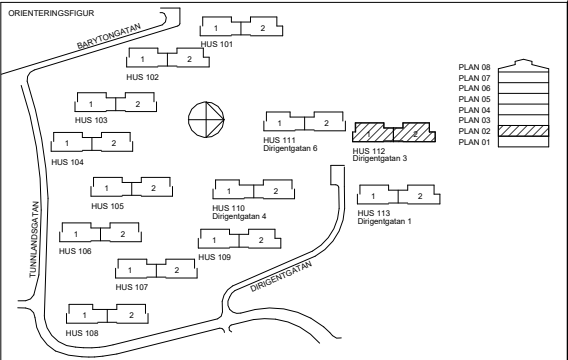

TOTALENTREPRENÖR

SKANSKA

010-448 00 00

**BOSTADS AB
POSEIDON**

Box 1 (Ångers Torg 14)
424 21 Ångers
Orgnr: 556120-3398

DISTRIKT:
Väster, Mandolingatan 116

PROJEKTNUMMER
906164

GATUADRESS
Dirigentgatan 1, 3, 4, 6

FASTIGHETSNUMMER
5837

CAD
Revit
2020

SKALA
A1
A3

NUMMER
A--40-1-1202000

BET

BET		ÄNDRINGEN AVSER		DATUM		SIGN	
BYGGHANDLING							
STAMRENOVERING KAVERÖS 4ST HUS JÄRNBROTT 154:1							
☒	A	STUDIO EKBERG AB			0709-36 06 90		
	AK	CEDÅS AKUSTIK			070-515 40 58		
	BR	AFRY			010-505 32 06		
	E	ESF SERVICE			031-54 54 22		
	VS	BENGT DAHLGREN			031-720 25 00		
	V	ENERGI & MILJÖTEKNIK			031-69 61 00		
URSPRUNGSARKITEKT GAKO Arkitektkontor							
UPPDRAG NR		RITAD/KONSTR AV		HANDLÄGGARE			
SKAD2501		PP		P PODDA			
DATUM		ANSVARIG					
2025-03-31		CHARLOTTE FLODIN					
ÖVERSIKTSPLAN							
HUS 112							
PLAN 02, ENTRÉPLAN							
CAD		SKALA		NUMMER		BET	
Revit		A1		A--40-1-1202000			
2020		A3					

C:\Users\peter.podda\Documents\Hus_112_NYT11 UTSEENDE_2021_0211\Hus_112_NYT11 UTSEENDE_2021_0211.dwg