DIRIGENTGATAN 4

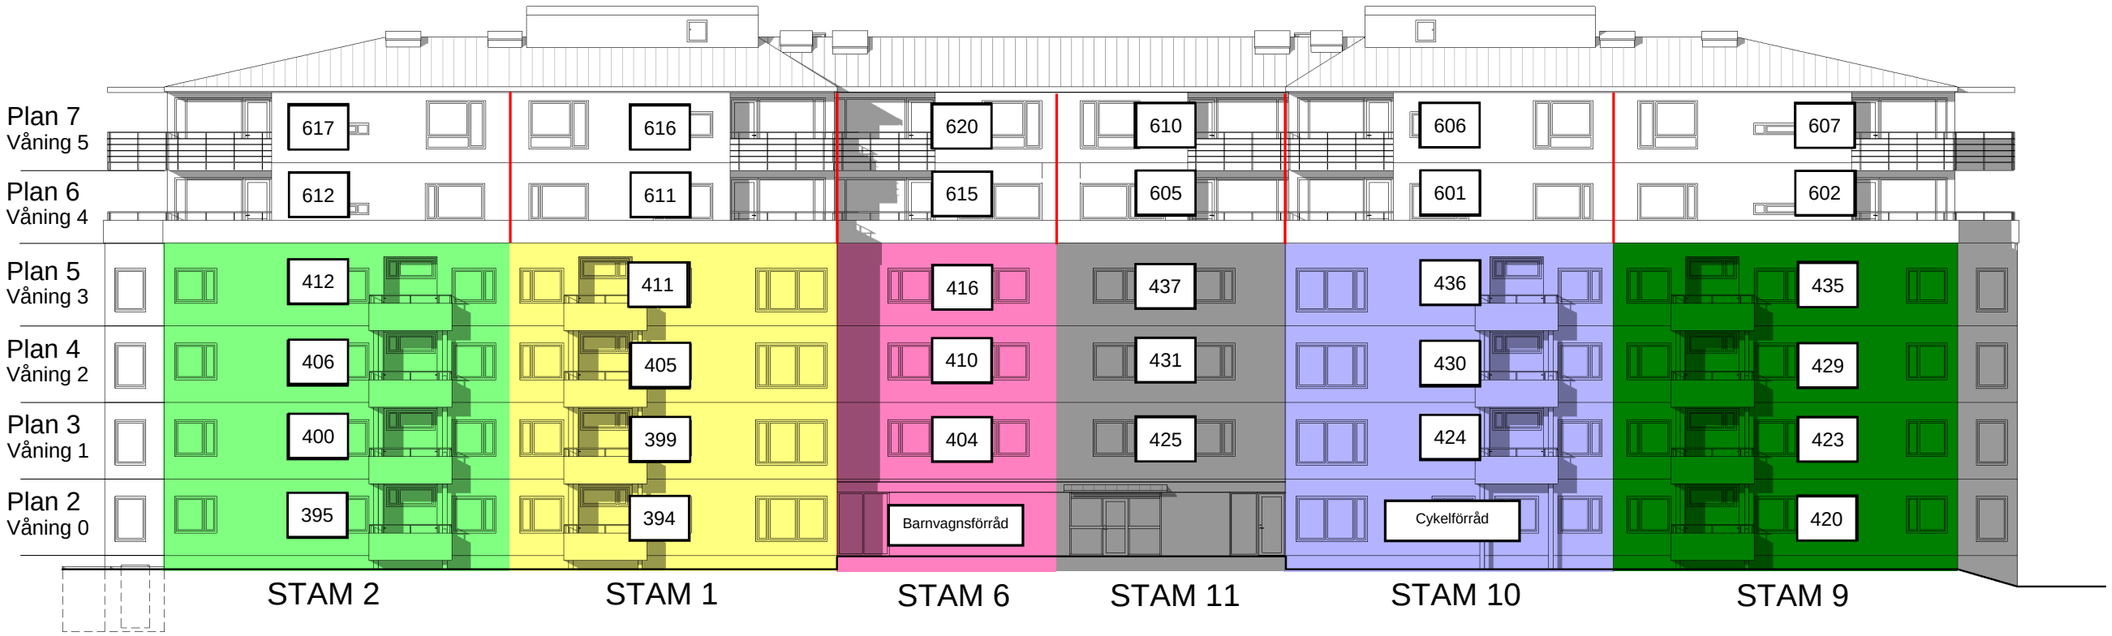

FASAD MOT VÄSTER

ENTRÈ

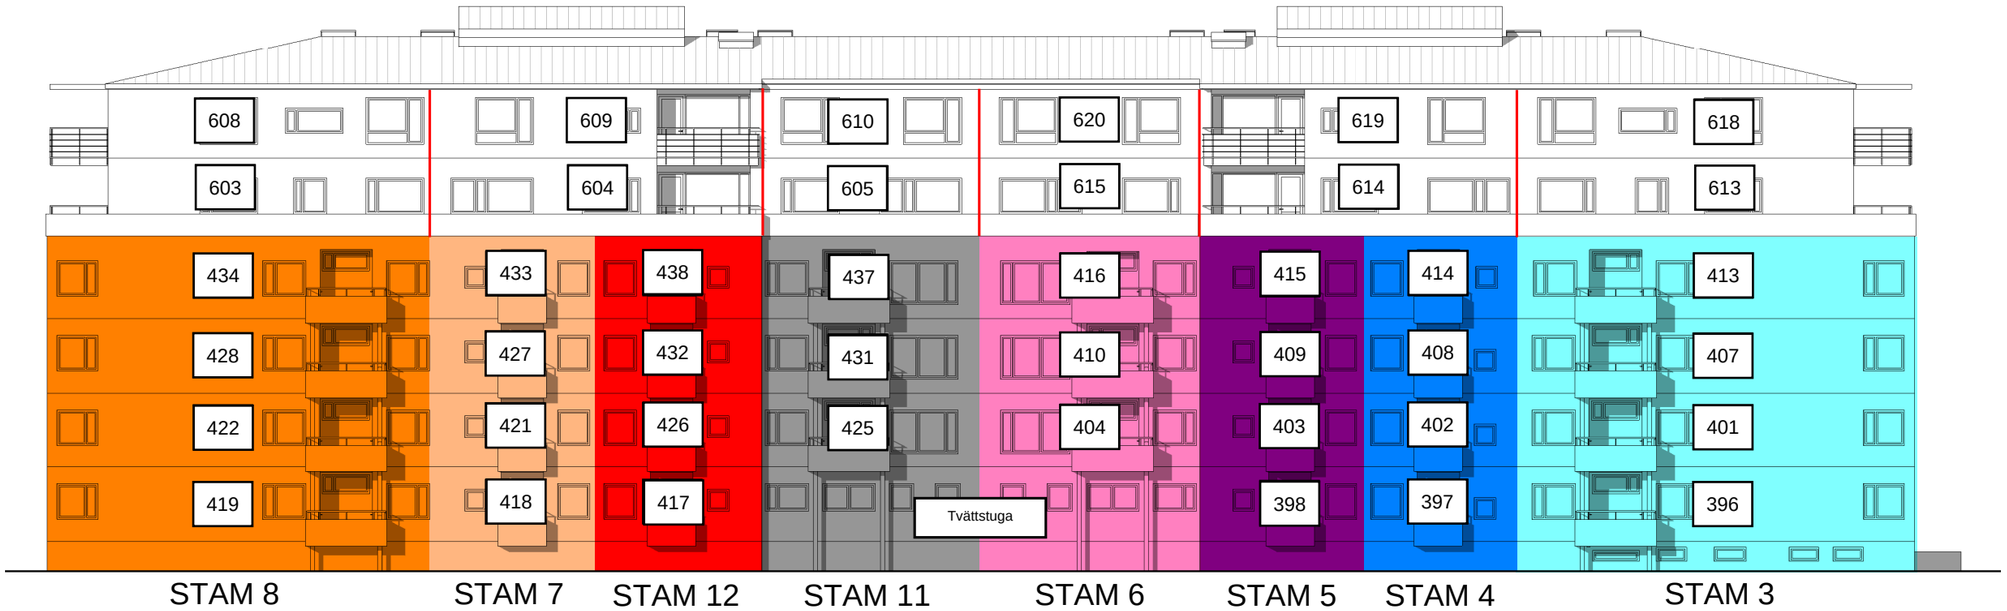

FASAD MOT ÖSTER

BAKSIDA